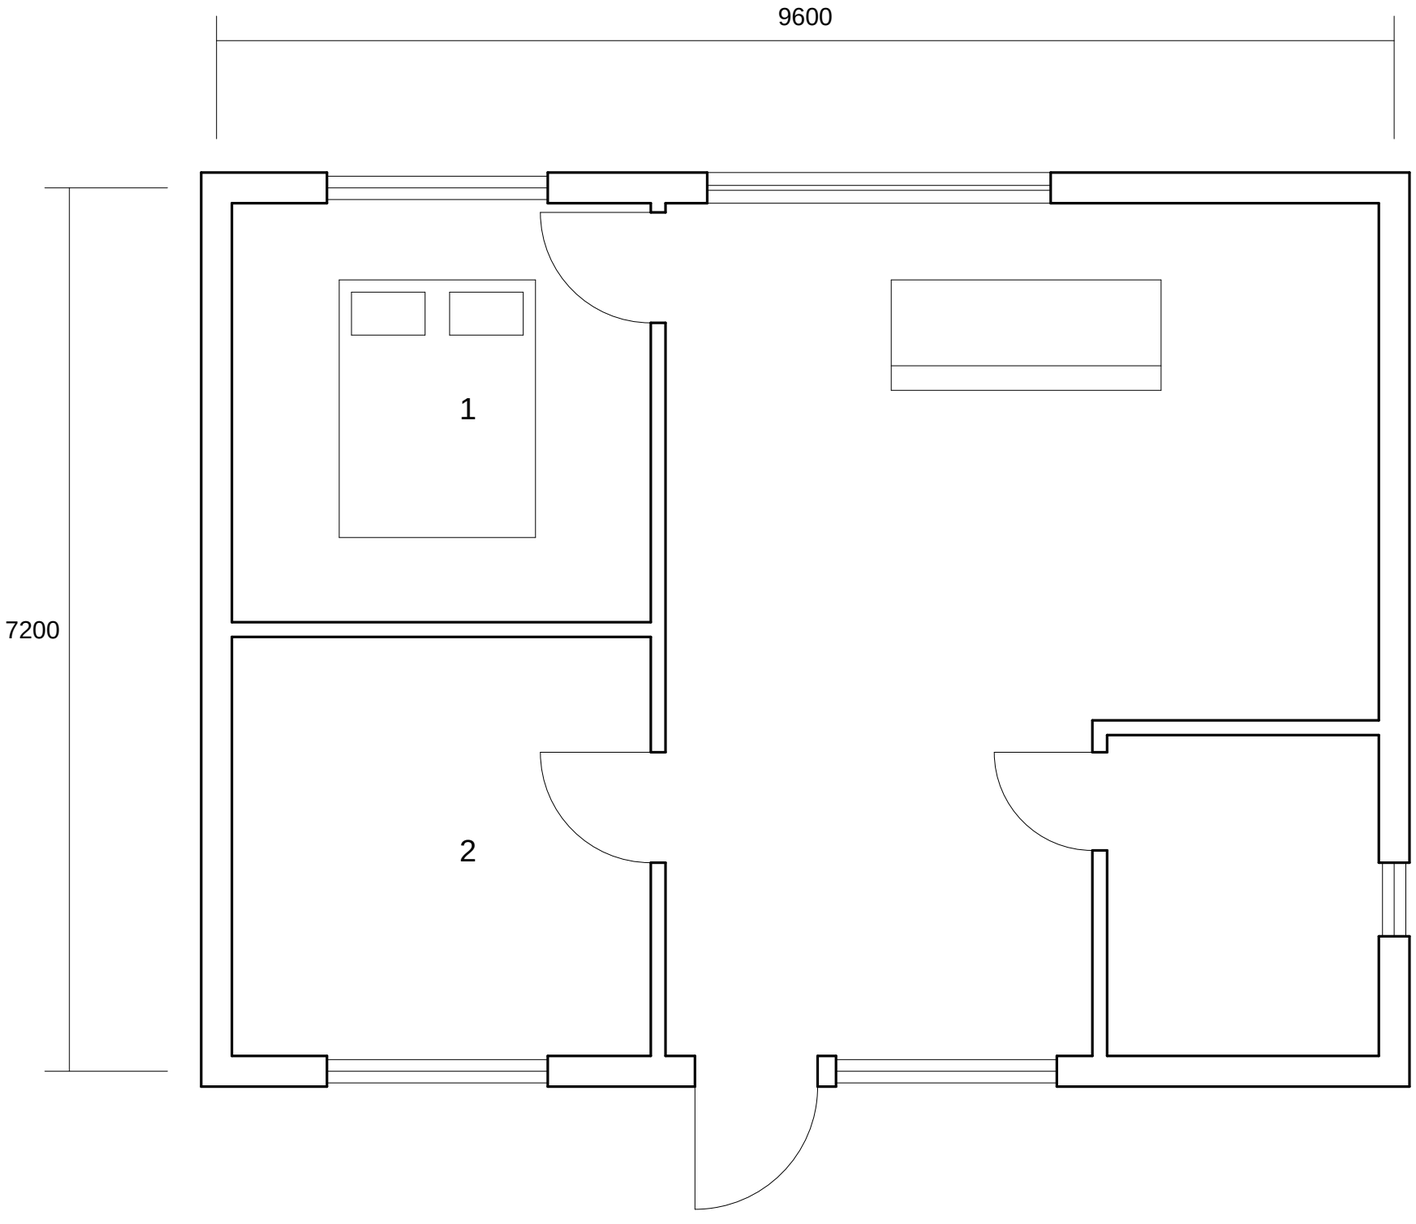
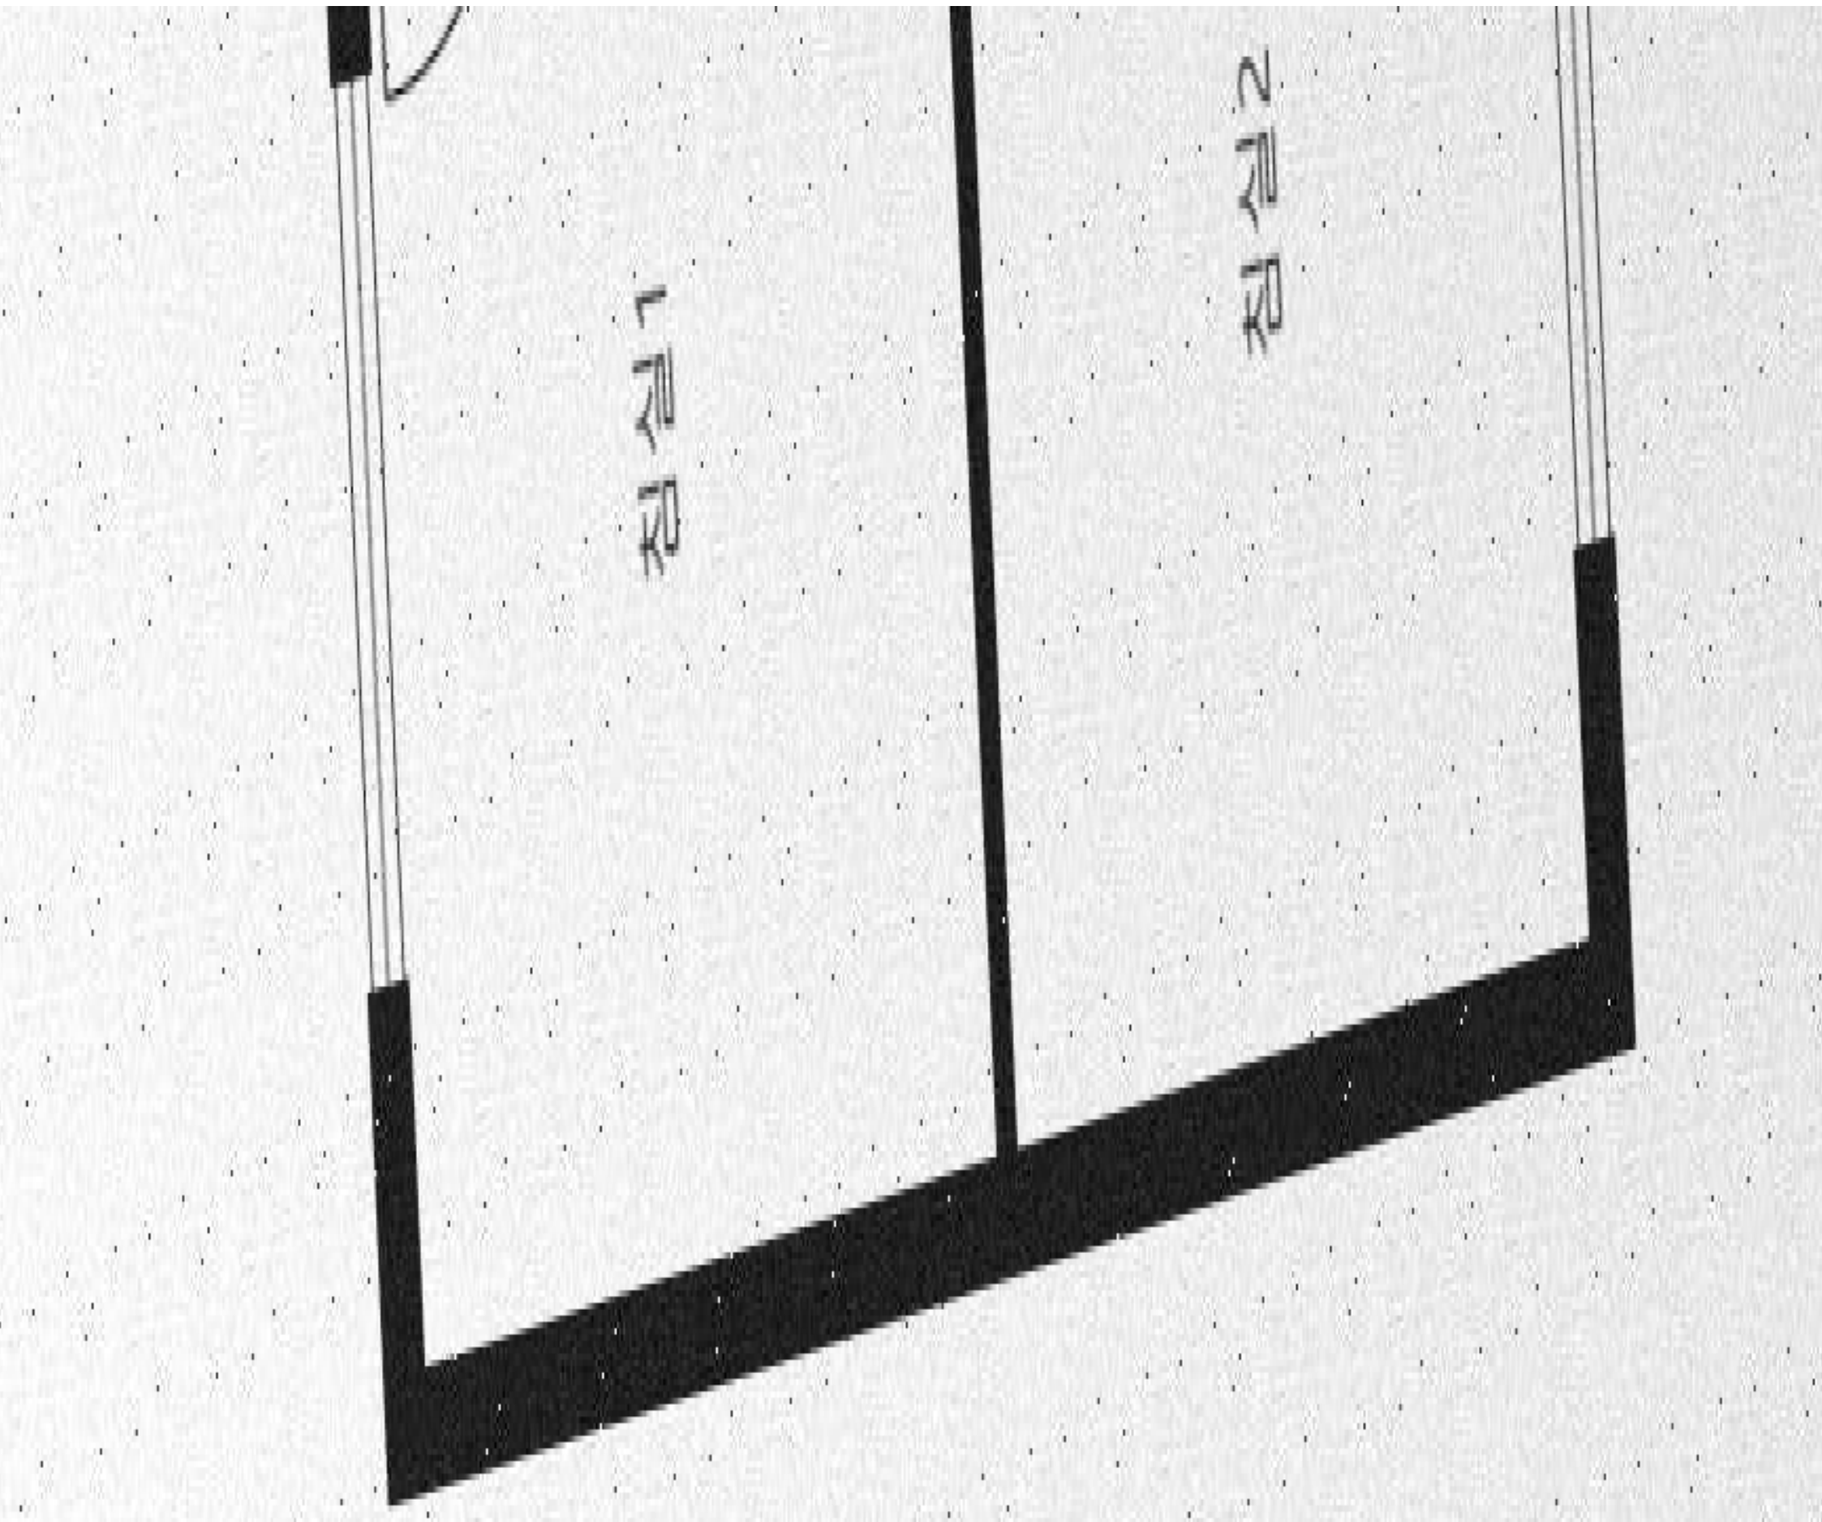


APARTMENT 59 - FLOOR PLAN

SCALE 1:50


KD 212
KD 212